



Λάμπρου Αικατερίνη

portfolio.

2025

Τα project που ακολουθούν έχουν πραγματοποιηθεί κατά τη διάρκεια φοίτησης μου στο Πανεπιστήμιο Δυτικής Αττικής για τα μαθήματα **Αρχιτεκτονική Εσωτερικών Χώρων** και **Εχεδιασμός Εξωτερικών Χώρων**, σε συνεργασία με συμφοιτητές μου.

Μπορείτε να δείτε τα ολοκληρωμένα project με όλες τις πληροφορίες τους στον λογαριασμό μου στο **GitHub**:

<https://github.com/KaterinaLambrou/University-Projects>

Fragments of a mirage; Revealing the bearing structure | Στοά Ανατολής
Sunset Dwelling A sunset inspired cave residence | Οία
Stich & Stone An ottoman house revived as a sewing atelier | Συκιά
The Kiln Hub A factory reborn as a community space | Νέα Μάκρη
Interstice Between restoration and reinterpretation | Αθήνα


Fragments of a mirage; Revealing the bearing structure

Η Στοά Ανατολής, αποτελούμενη από τη **σύνθεση δύο όγκων**, αποτελεί την πρώιμη μορφή της Αθηναϊκής στοάς. Στον ημιυπαίθριο και υπόγειο χώρο της εκτυλλίζονται καταστήματα με **διαφορετικές στιλιστικές ταυτότητες**, όπου με την πάροδο των χρόνων η αλλαγή και η προσθήκη στρώσεων υλικών έχει μετατρέψει την Στοά σε **παλίμψηστο**.


Το κέντρο επανασχεδιασμού αυτής της στοάς αποτελεί η **αντιστροφή του παλίμψηστου**, απογυμνώνοντας το κτίριο και διατηρώντας την σημαντικότερη στρώση του, τον **φέρων οργανισμό**. Στόχος του σχεδιασμού αποτέλεσε η ανάδειξη της φέρουσας τοιχοποιίας, το οποίο επιτεύχθηκε μέσω της χαρακτηριστικής **αντανάκλασης του καθρέπτη**.



Η νέα χρήση της Στοάς πρόκειται για **βοηθητικό χώρο του ΕΚΠΑ**, φιλοξενώντας χώρους όπως βιβλιοθήκη, αναγνωστήριο, βοηθητικό πωλητήριο βιβλίων του Εύδοξου, αλλά και χώρο εκθέσεων, καφετέρια κ.α.

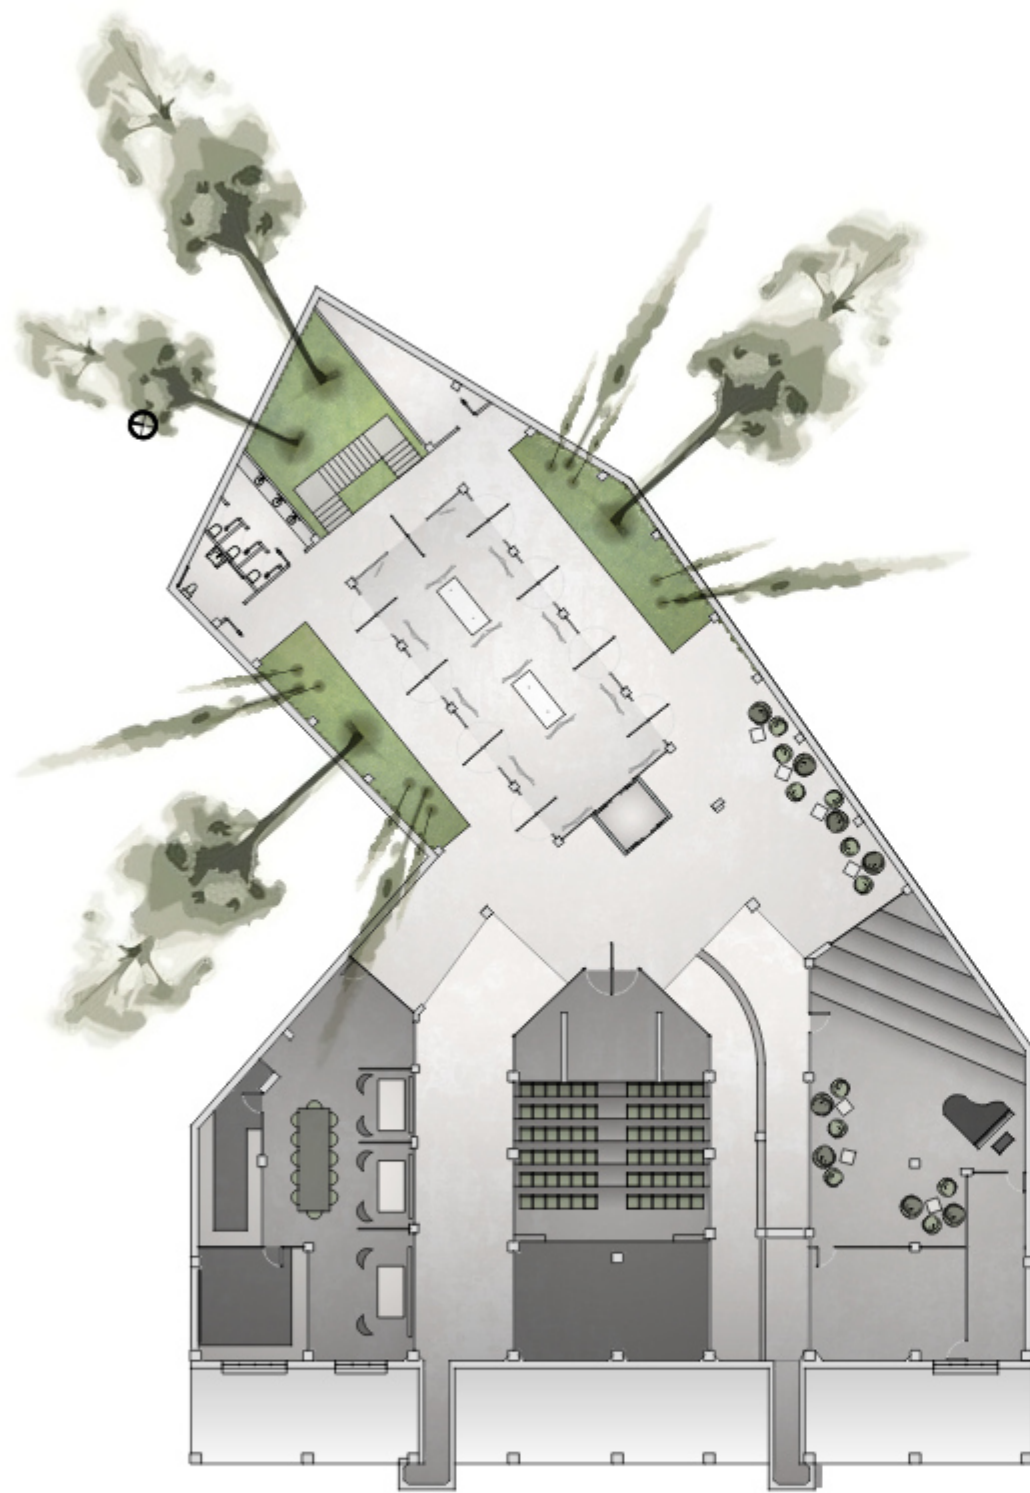

ΚΑΤΩΛΗ ΥΠΟΓΕΩΥ
ΣΤΟΑΣ ΑΝΑΤΟΛΗΣ

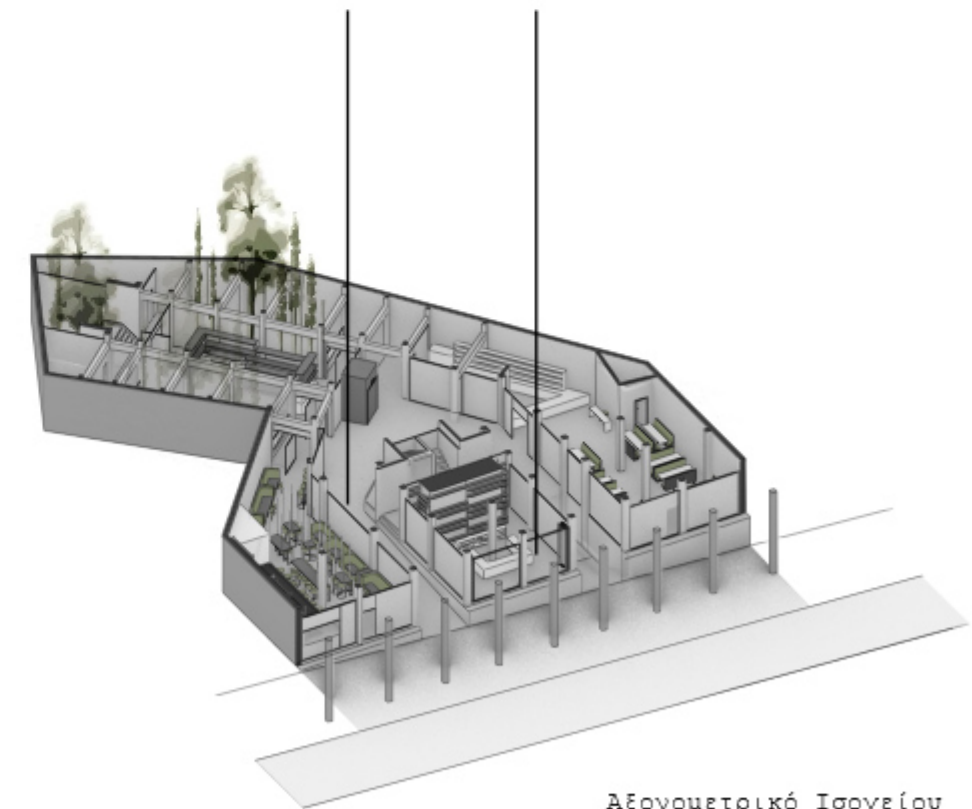

Αξονομετρικό Ισογείου

Ισόγειο



Τρίτος
όροφος



Υπόγειο



Δεύτερος
όροφος



Διάδρομος
υπογείου



Πρώτος
όροφος



Sunset Dwelling

A sunset inspired cave residence

Η Οία αποτελεί έναν παραδοσιακό διατηρητέο οικισμό στο βόρειο άκρο της Σαντορίνης. Στον ανασχεδιασμό της συγκεκριμένης **υπόσκαφης κατοικίας**, κεντρική ιδέα αποτελεί η **κίνηση του ηλίου** όπως και τα **χρώματα του ηλιοβασιλέματος**.


Στην κάτοψη κυριαρχεί μια **καμπύλη κίνηση** η οποία αποτελεί καθοριστικό στοιχείο χωροθέτησης, είτε παίρνοντας μορφή επίπλων είτε διαχωριστικών. Η **σταθερή επίπλωση είναι χτιστή** και σχεδιασμένη ειδικά για αυτόν τον μοναδικό χώρο.






ΟΨΗ
ΚΑΛΥΜΑΚΑ 1:20



ΤΟΜΗ B-B
ΚΑΛΥΜΑΚΑ 1:20

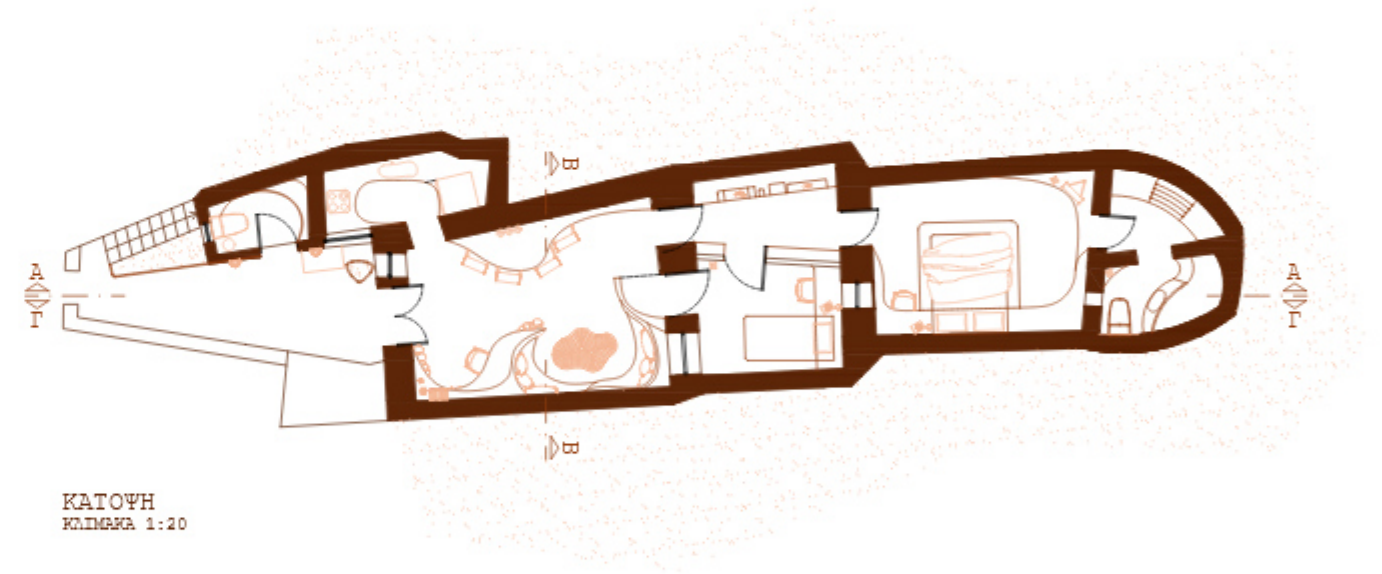

ΚΑΤΟΨΗ
ΚΑΛΥΜΑΚΑ 1:20

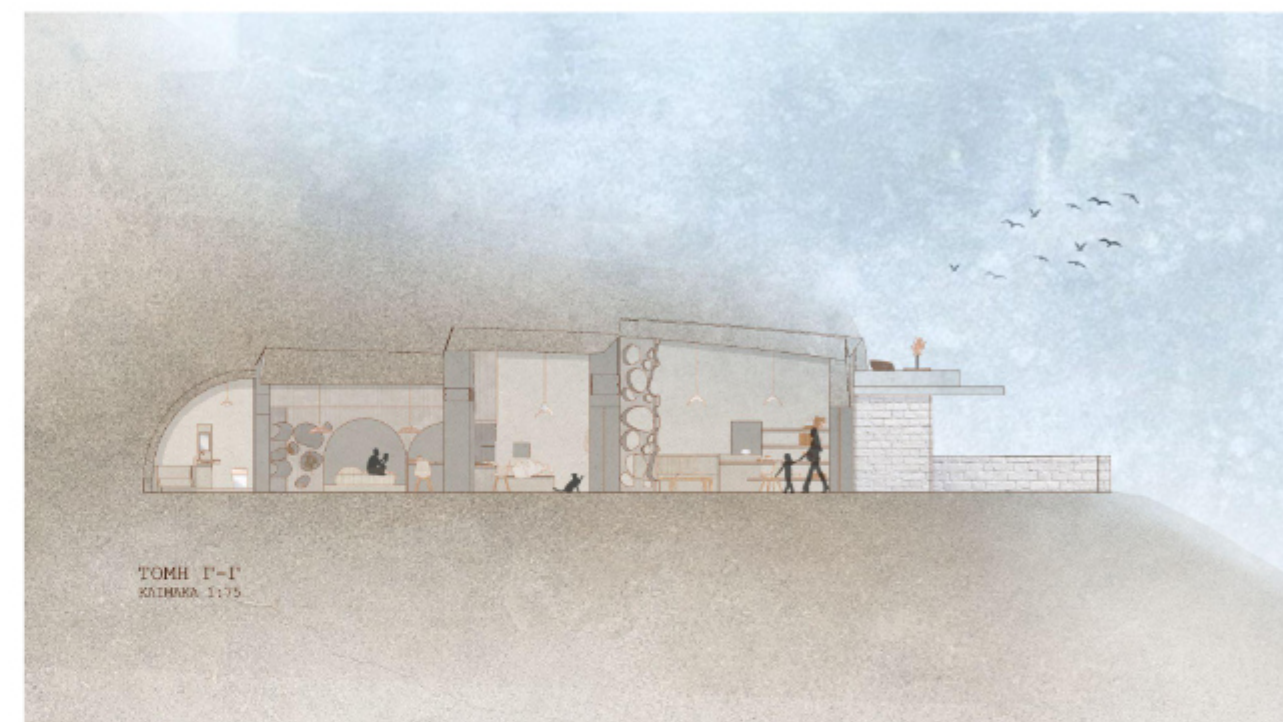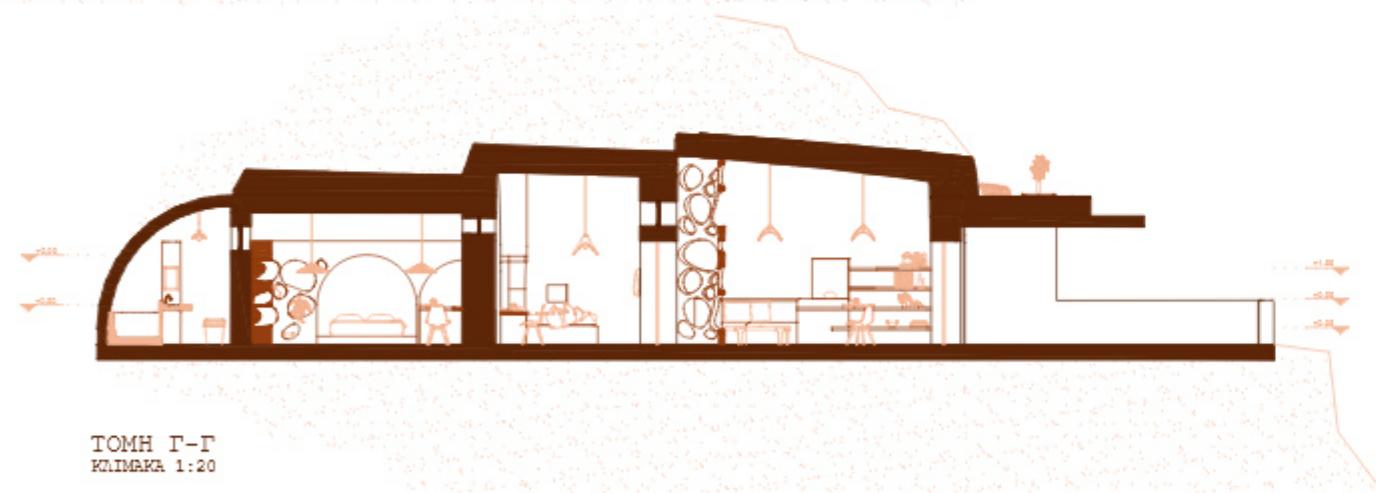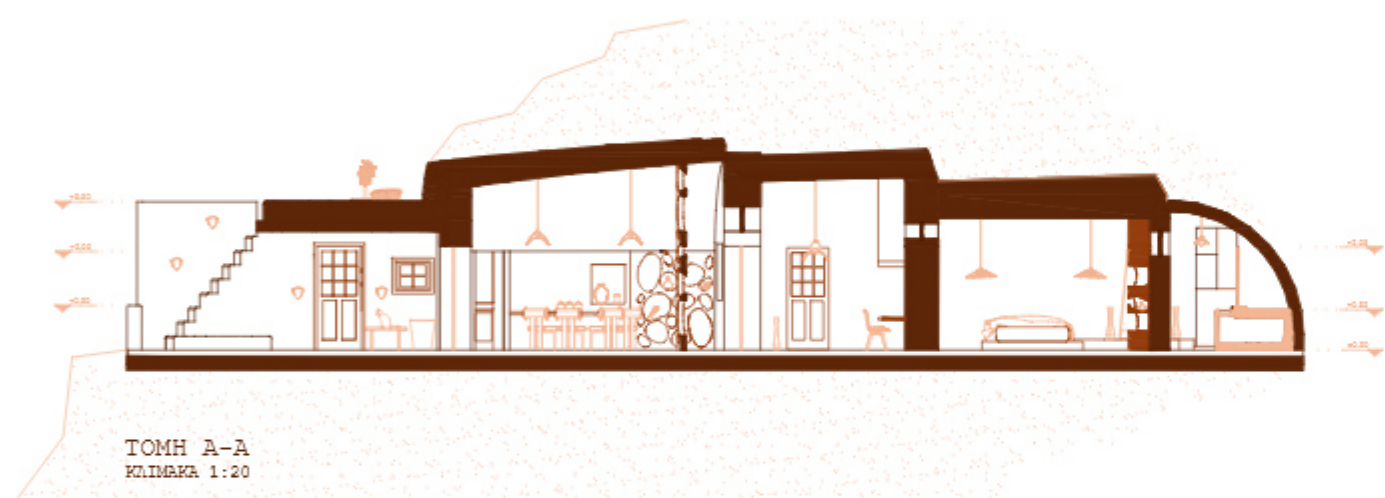

Είσοδος



Διάδρομος
Ιδιωτικών χώρων



Γραφείο
Καθιστικό



Διάδρομος
Ιδιωτικών χώρων



Τραπεζαρία
διάδρομος



Master
Υπνοδωμάτιο





Stich & Stone

An ottoman house revived
as a sewing atelier

Το **οθωμανικό πυργόσπιτο** Κιαμήλ Μπέη βρίσκεται στην Συκιά και αποτελείται από **2 επίπεδα**. Διαθέτει κεραμοσκεπή, τοξωτά ανοίγματα, προεξωχές τζακιών όπως και έναν εξώστη στην βορειοανατολική του όψη.


Για τη μελέτη επανάχρησης σε κτίριο δημόσιου χαρακτήρα, επιλέχτηκε σχεδιαστεί ως **συνεργατικό εργαστήριο ραπτικής με χώρο πωλητηρίου**.

Η επέμβαση που πραγματοποιήθηκε αποσκοπεί να **μην αλλοιώσει την αυθεντική ταυτότητα του χώρου**. Διατηρούνται τα καμπύλα στοιχεία, ο διάκοσμος όπως και η εκτεταμένη χρήση ξύλου, με αίσθηση μιμούμενη της **σύγχρονης μίνιμαλ αρχιτεκτονικής**.

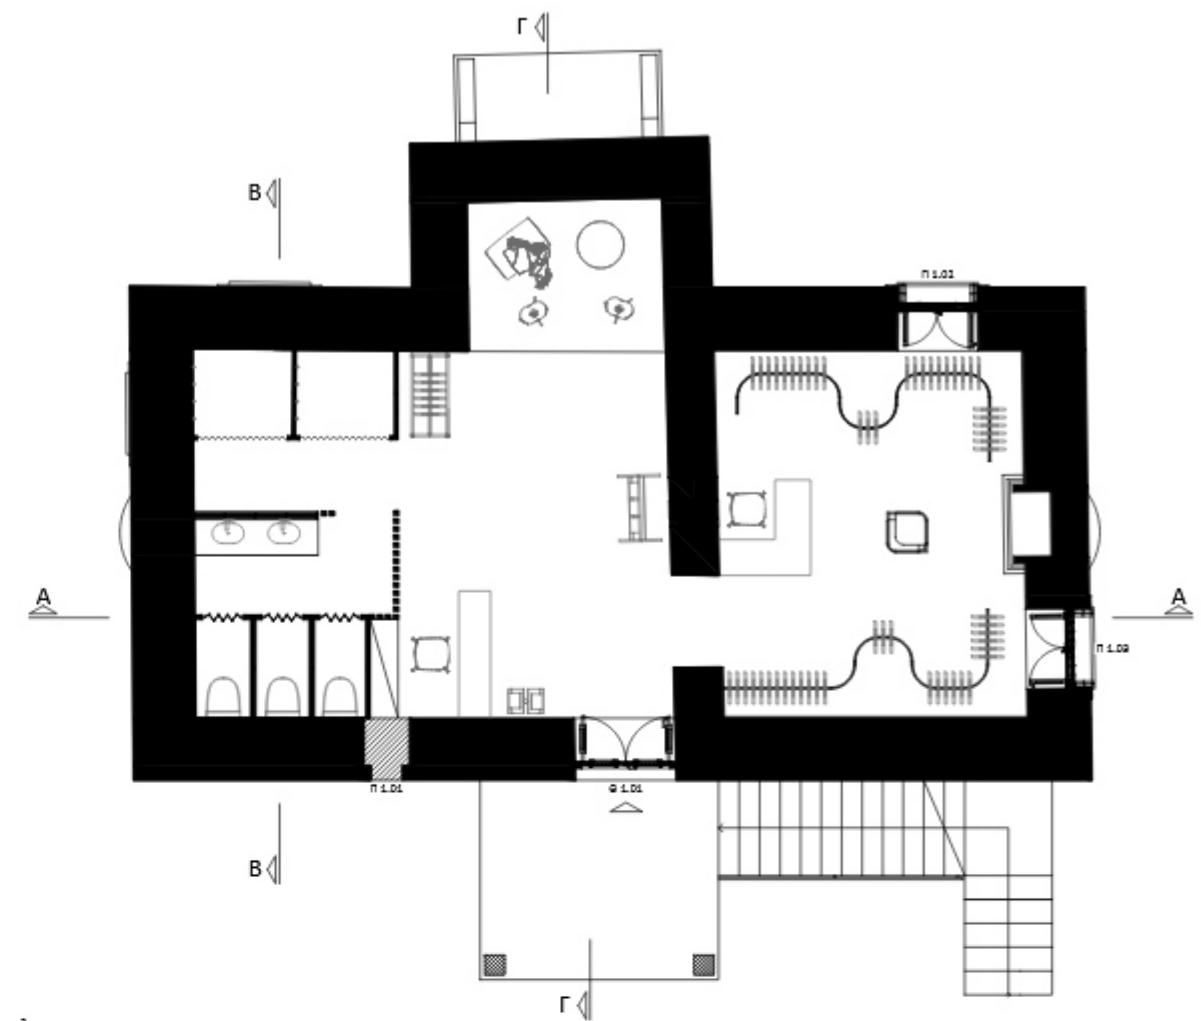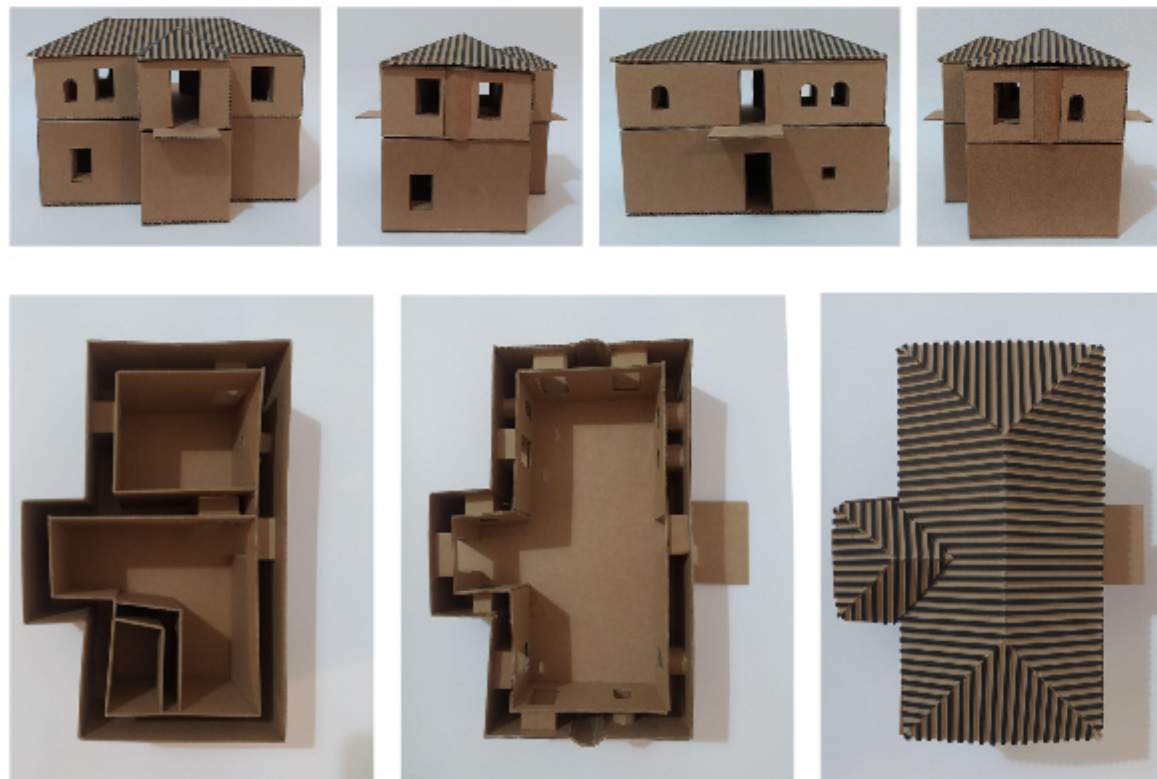


ΥΠΛΟΔΑ - ΕΦΑΚΟΡ / ΣΧΕΔΙΑ Μ. ΔΗΜΗΤΡΟΠΟΥΛΟΥ

ΚΑΤΩΗ ΙΣΟΓΕΙΟΥ
κλ. 1:20

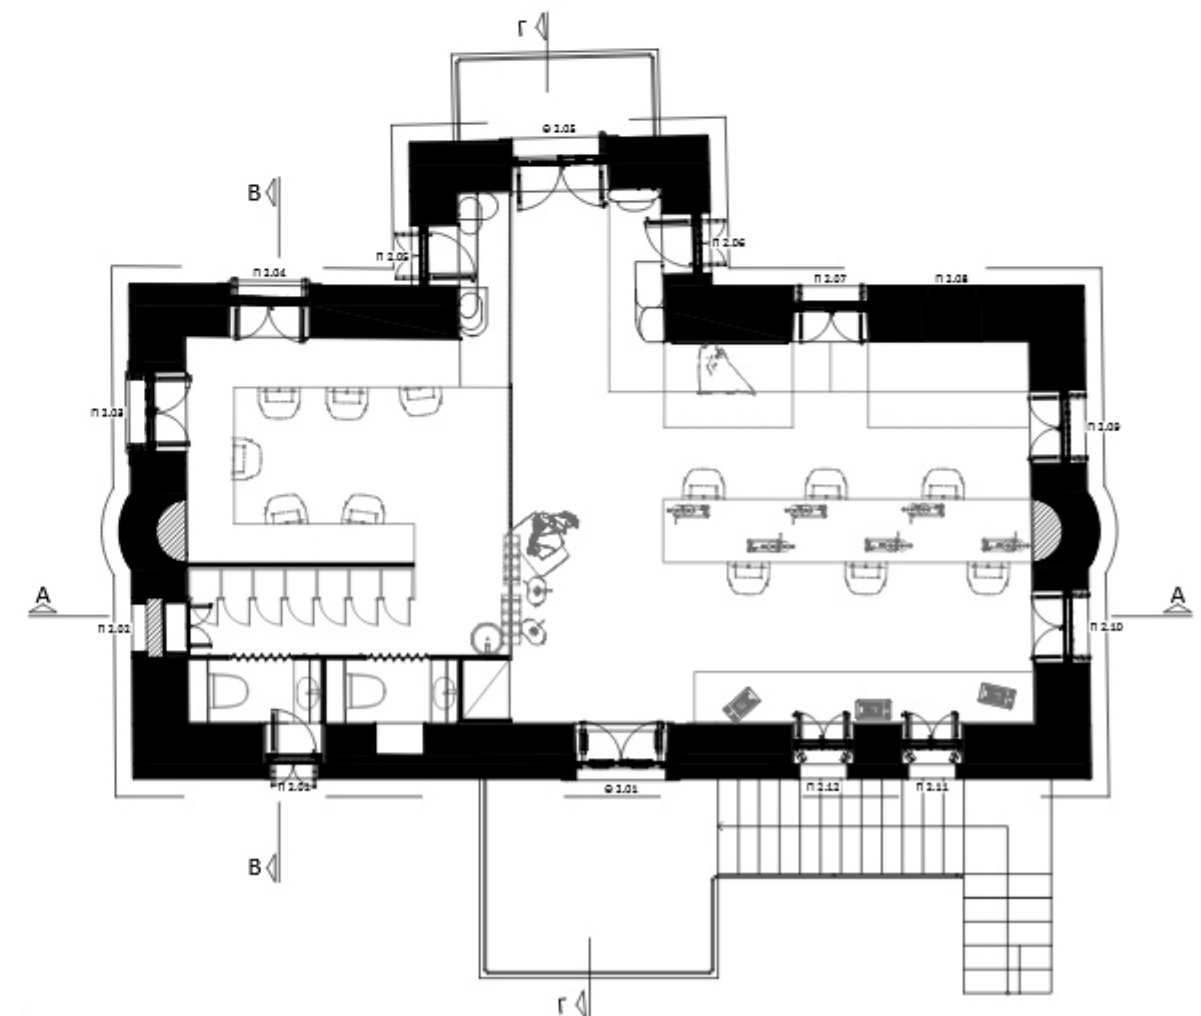


ΥΠΛΟΔΑ - ΕΦΑΚΟΡ / ΣΧΕΔΙΑ Μ. ΔΗΜΗΤΡΟΠΟΥΛΟΥ

ΚΑΤΩΗ ΟΡΟΦΟΥ
κλ. 1:20

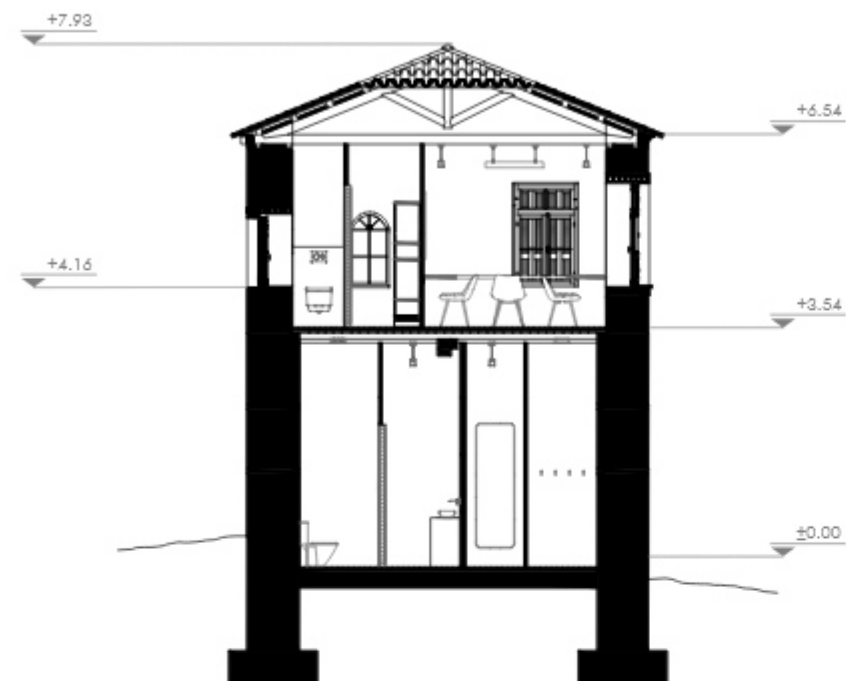

ΥΠΟΔΑ - ΕΦΑΚΟΡ / ΣΧΕΔΙΑ Μ. ΔΗΜΗΤΡΟΠΟΥΛΟΥ

ΤΟΜΗ Β - Β
1:100

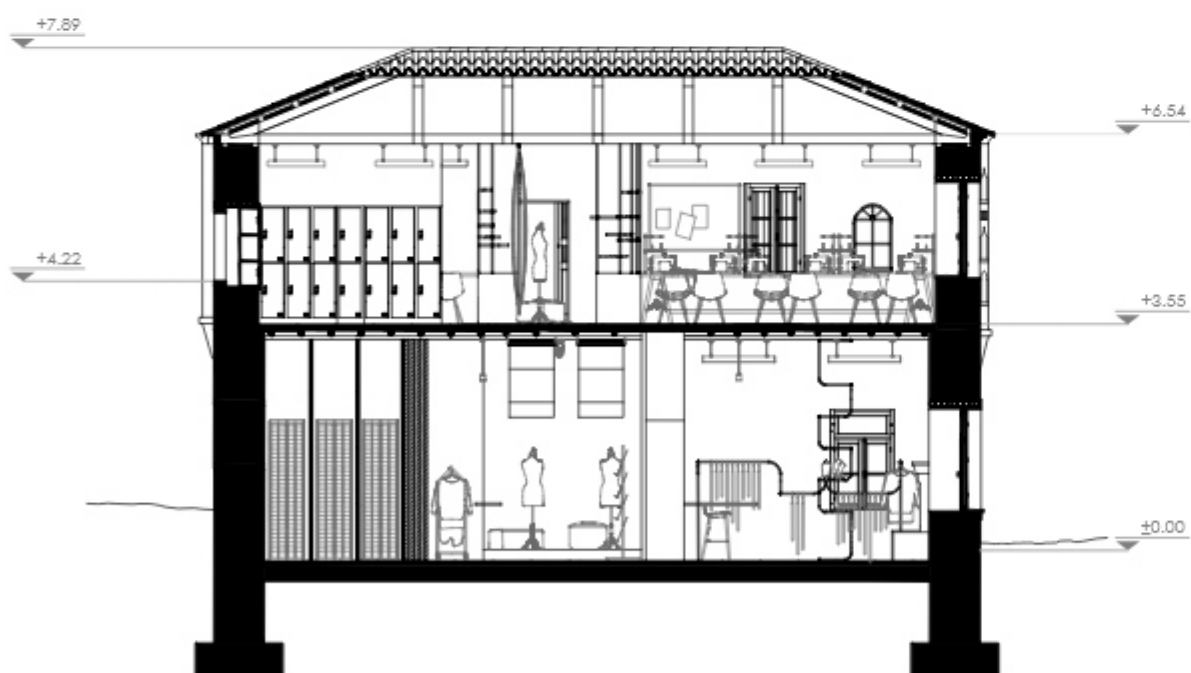


ΥΠΟΔΑ - ΕΦΑΚΟΡ / ΣΧΕΔΙΑ Μ. ΔΗΜΗΤΡΟΠΟΥΛΟΥ

ΤΟΜΗ Α - Α
1:100



Ισόγειο
Ρεσεψιόν

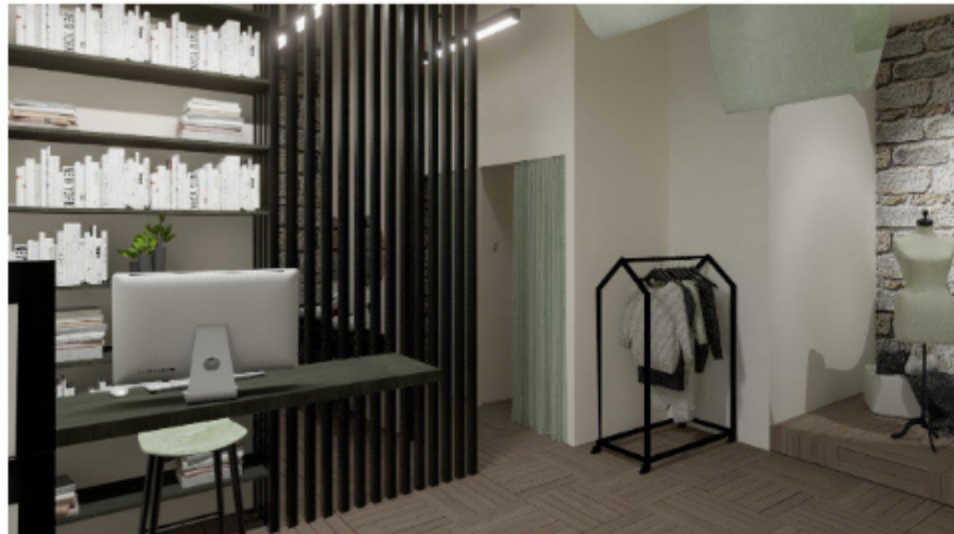

Ισόγειο
Βιτρίνα



Ισόγειο
Πωλητήριο



Ισόγειο
Πωλητήριο



Όροφος
Πάγκοι
ραπτικής



Όροφος
Πάγκοι
σχεδίασης



Όροφος
χώρος υλών



Όροφος
WC



The Kiln Hub

A factory reborn as a community space


Το εργοστάσιο πορσελάνης στη Νέα Μάκρη κτίστηκε το 1950, ενώ ανέστειλε τη λειτουργία του το 1969. Αποτελείται από δύο όγκους, έναν ορθογώνιο με οδοντωτή στέγη και έναν στενό σε σχήμα Γ. Στην εργασία αυτή επιλέχθηκε ο επανασχεδιασμός του ορθογώνιου τμήματος.

Κεντρική ιδέα για τον σχεδιασμό του χώρου αποτελεί η μετάβαση από το παρελθόν στο παρόν. Υλοποιείται με τη δημιουργία ενός περάσματος, σηματοδοτώντας μια πορεία που γίνεται αντιληπτή μέσα από τη διαφοροποίηση του χώρου από στενό και ιδιωτικό, σε μια πορεία προς το ευρύχωρο και διαπερατό.


Το παρελθόν έχει αισθητικά περισσότερη φασαρία και είναι πιο ασφυκτικό, ενώ η μετάβαση στο παρόν έχει μειωμένη πληροφορία και δημιουργείται ένα πιο ανοιχτό περιβάλλον. Η διάταξη προκύπτει μέσα από τη χάραξη δύο ευθειών που ξεκινούν από την αρχή του κτιρίου και απομακρύνονται στο τέλος αυτού.




Η νέα χρήση του κτιρίου πρόκειται για πολιτιστικό κέντρο με reception desk, πωλητήριο πορσελάνηνων ειδών δώρου, αμφιθέατρο, χώρο εκθέσεων, καφέ, βιβλιοθήκη και WC.

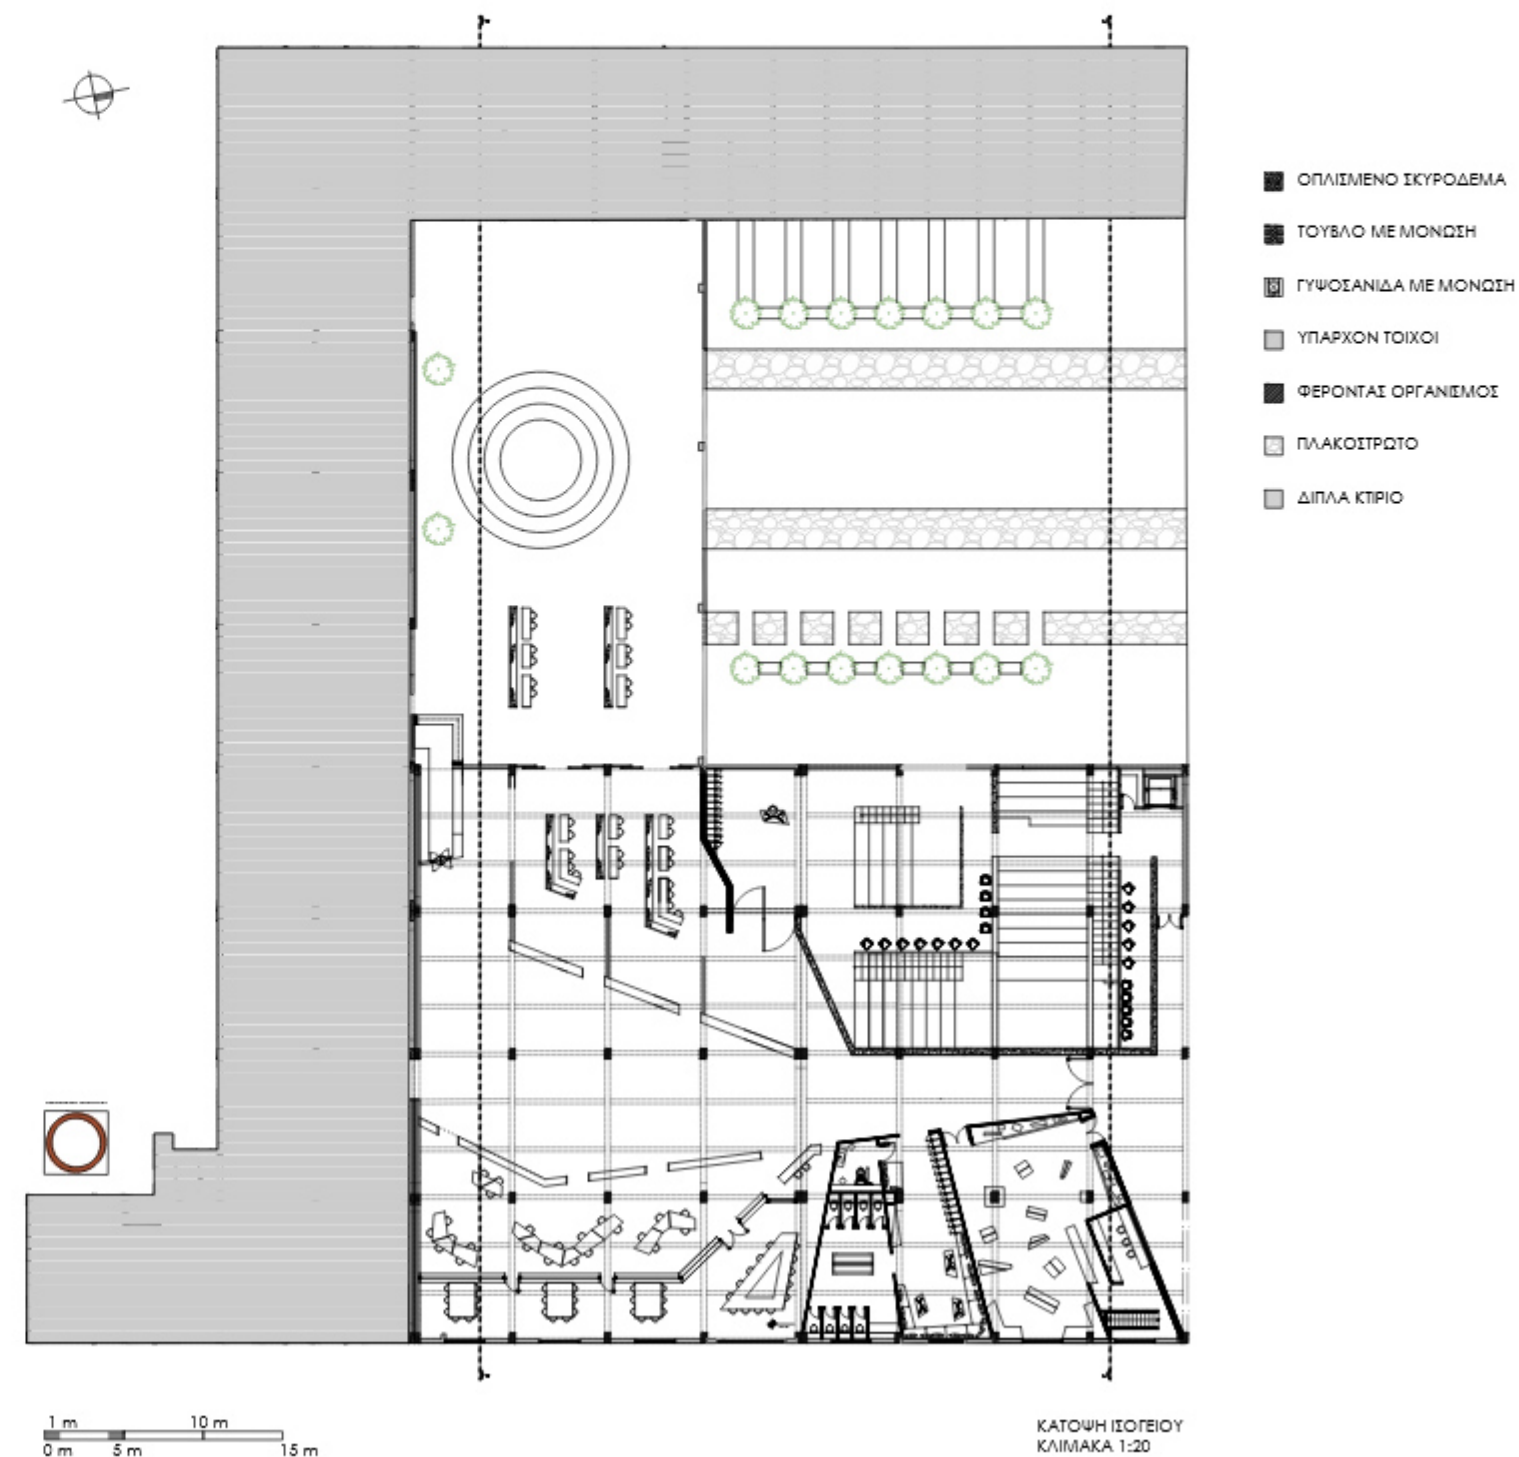

- ΟΠΛΙΣΜΕΝΟ ΣΚΥΡΟΔΕΜΑ
- ΤΟΥΒΛΟ ΜΕ ΜΟΝΩΣΗ
- ΓΥΦΟΣΙΑΝΙΔΑ ΜΕ ΜΟΝΩΣΗ
- ΥΠΑΡΧΟΝ ΤΟΙΧΟΙ
- ΧΩΜΑ

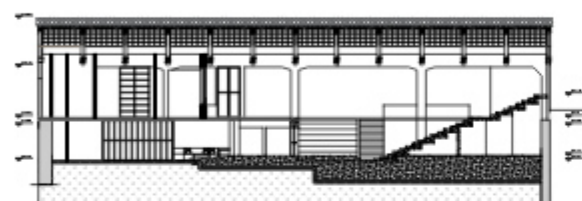


ΤΟΜΗ Α - Α

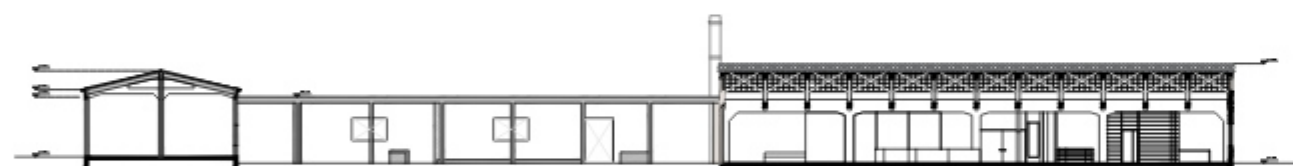

ΤΟΜΗ Β - Β

ΚΛΙΜΑΚΑ 1:20

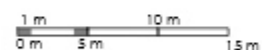

ΚΑΤΩΦΗ ΙΣΟΓΕΙΟΥ



ΤΟΜΗ Β-Β

Είσοδος
Πωλητήριο



Πωλητήριο



Διάδρομος
WC+lockers




Διάδρομος
Χώρος
εκθέσεων



Καφέ
Χώρος
εκθέσεων



Αμφιθέατρο

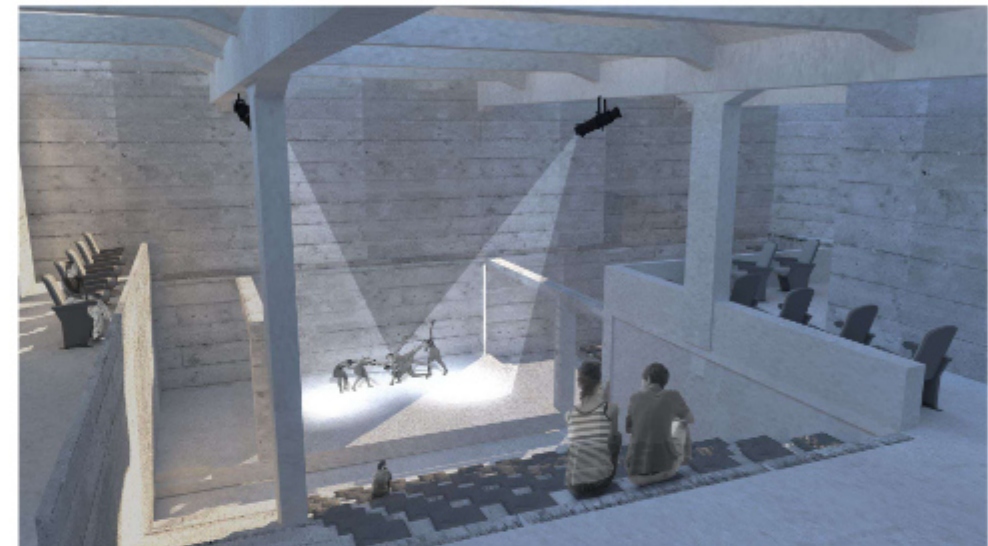

Αναγνωστήριο
Βιβλιοθήκη



Αναγνωστήριο
Βιβλιοθήκη



Interstice



Between restoration and reinterpretation

Το συγκεκριμένο project αφορά ένα νεοκλασσικό οικισμό με παραδοσιακή λιθοδομή, το οποίο επανασχεδιάζεται για να γίνει χώρος βραχυχρόνιας μίσθωσης Airbnb.

Η αρχιτεκτονική προσέγγιση βασίζεται στην ισορροπία μεταξύ διατήρησης και ανανέωσης, διαφυλάσσοντας τη μορφολογία και τα υλικά του αρχικού κελύφους. Ταυτόχρονα πραγματοποιούνται σύγχρονες επεμβάσεις οι οποίες ανταποκρίνονται στις ανάγκες της σύγχρονης κατοίκησης.



1. Ταμπλασωτή θύρα
2. Καρφωτή θύρα
3. Εξώφυλλα γερμανικού τύπου
4. Εξώφυλλα γαλλικού τύπου
5. Βυζαντινά κεραμίδια
6. Νεοκλασσικά φουρούσια

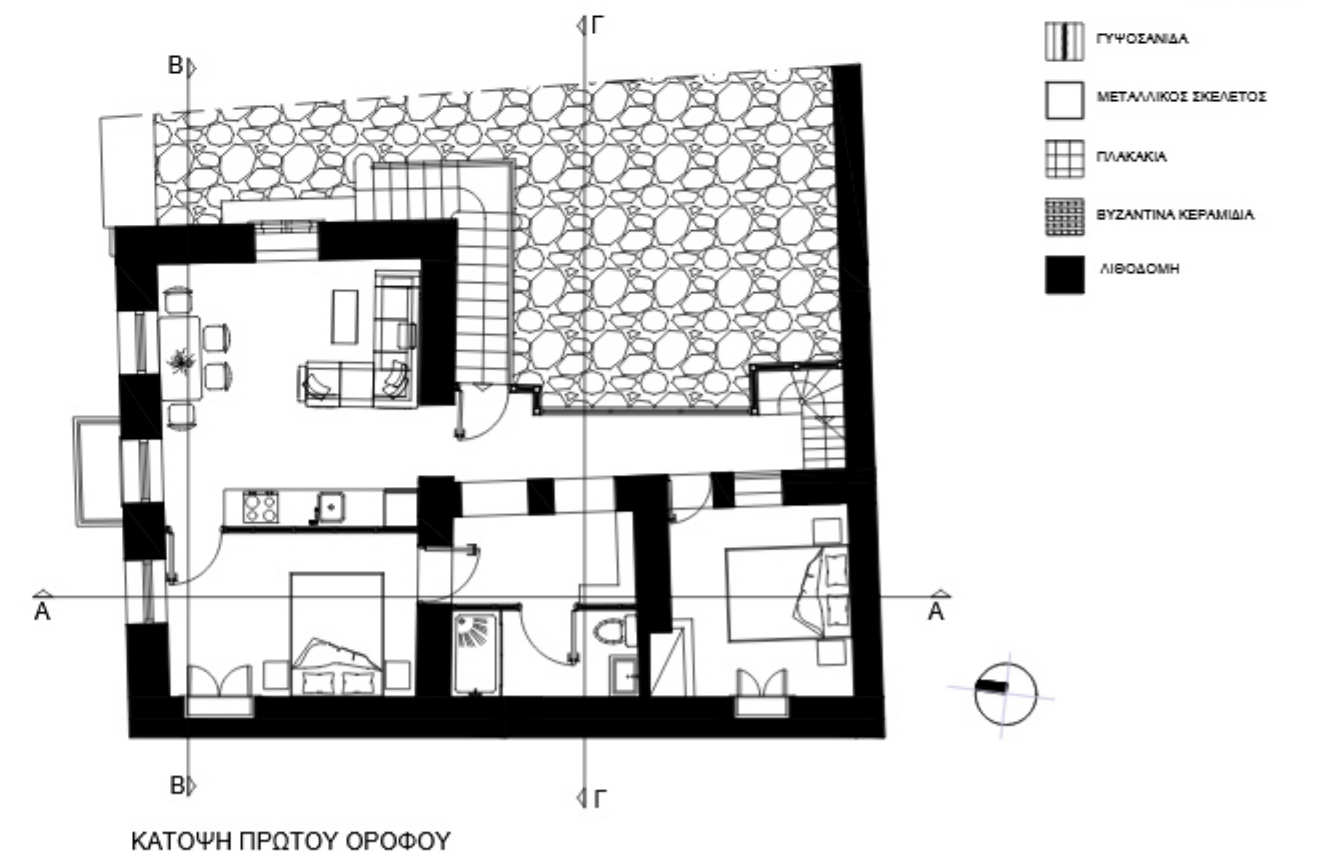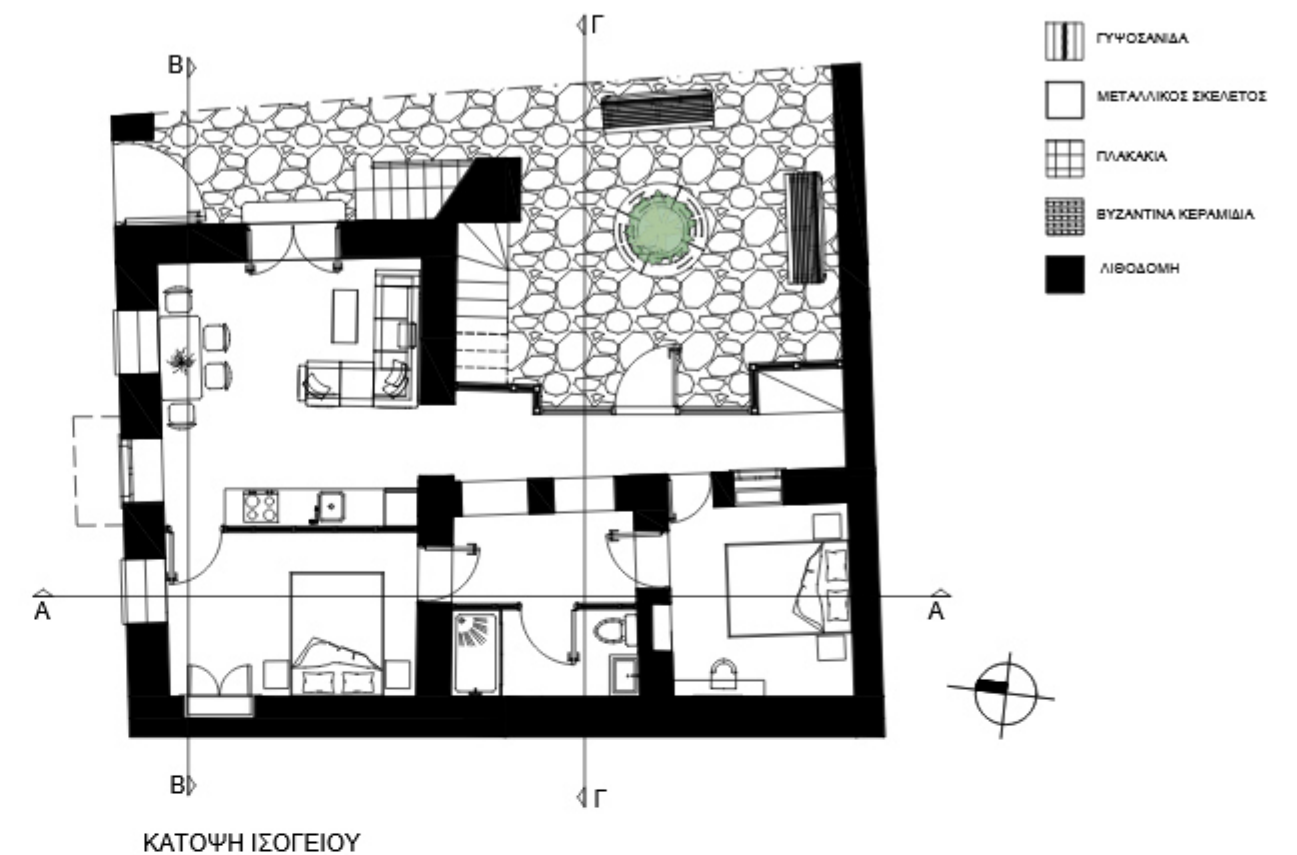


ΚΛΙΜΑΚΑ 1:20



ΚΛΙΜΑΚΑ 1:20




TOMH A-A

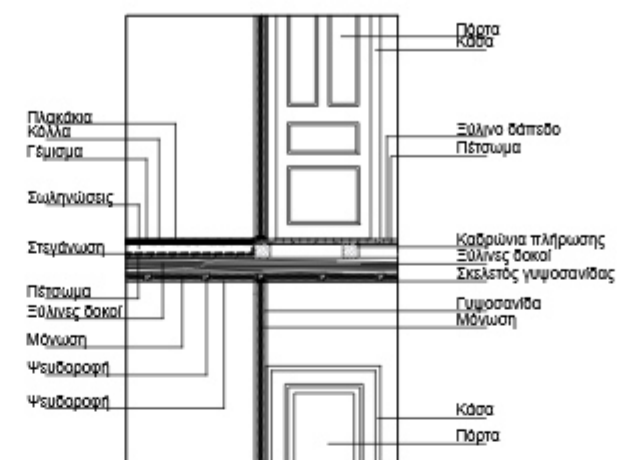


Λ5.1

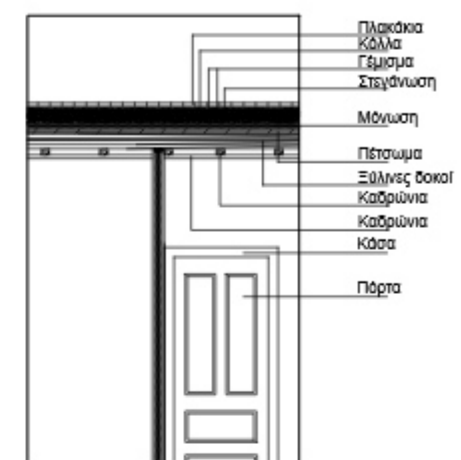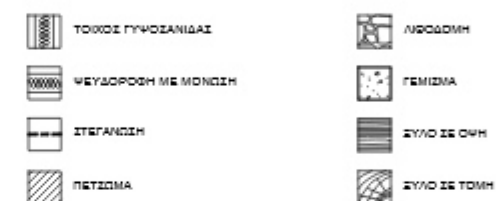


Λ5.2

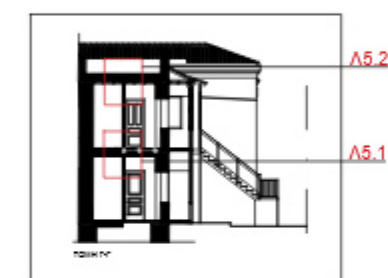


ΚΛΙΜΑΚΑ 1:10

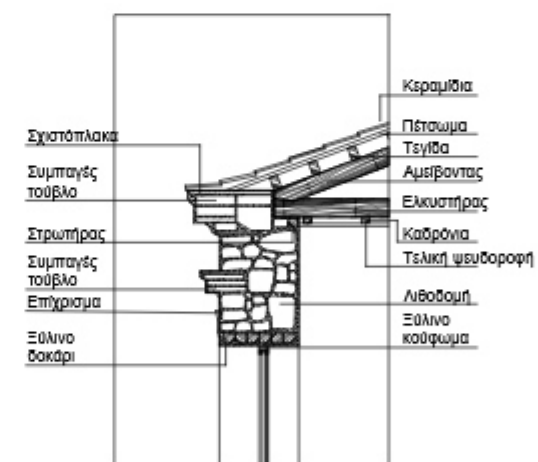




Λ3

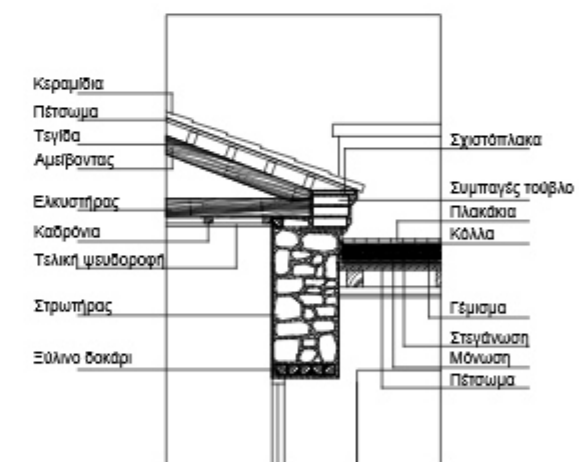

Λ4

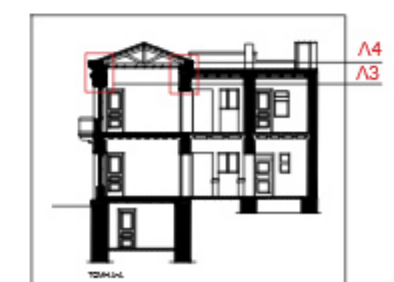

ΚΛΙΜΑΚΑ 1:10

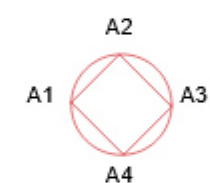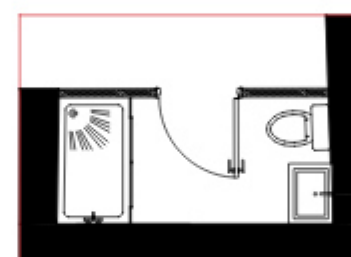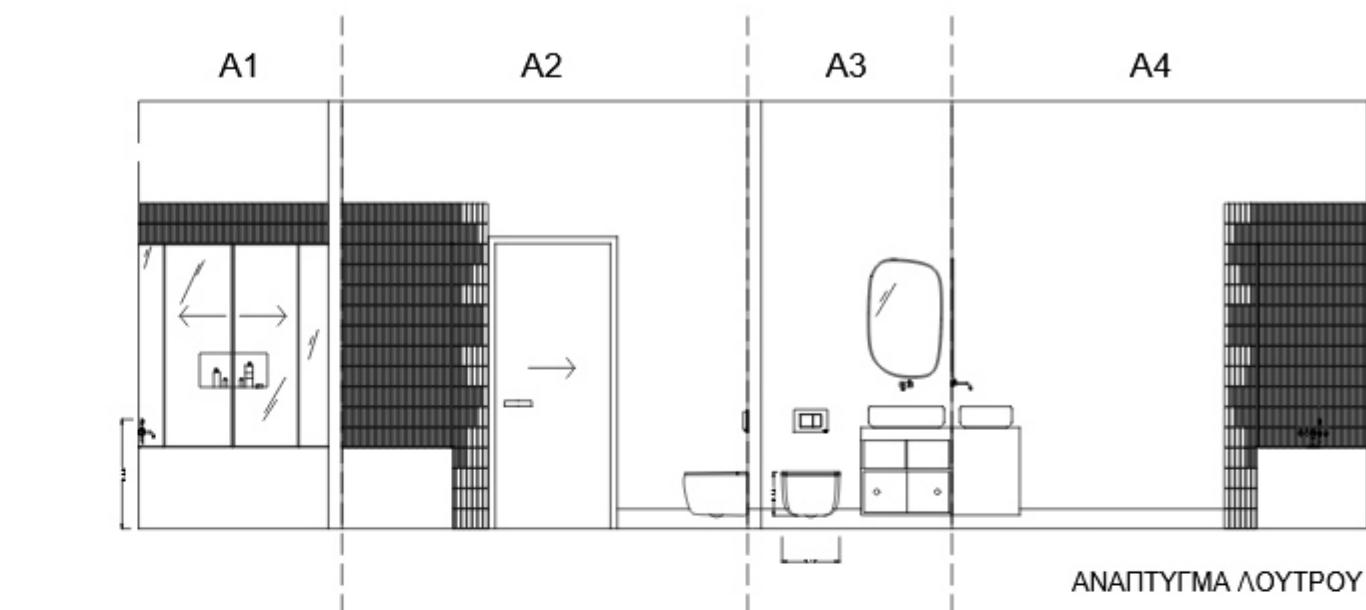

ΚΛΙΜΑΚΑ 1:10



ΑΝΑΠΤΥΓΜΑ ΛΟΥΤΡΟΥ